


1 2 3 4 5 6 7 8

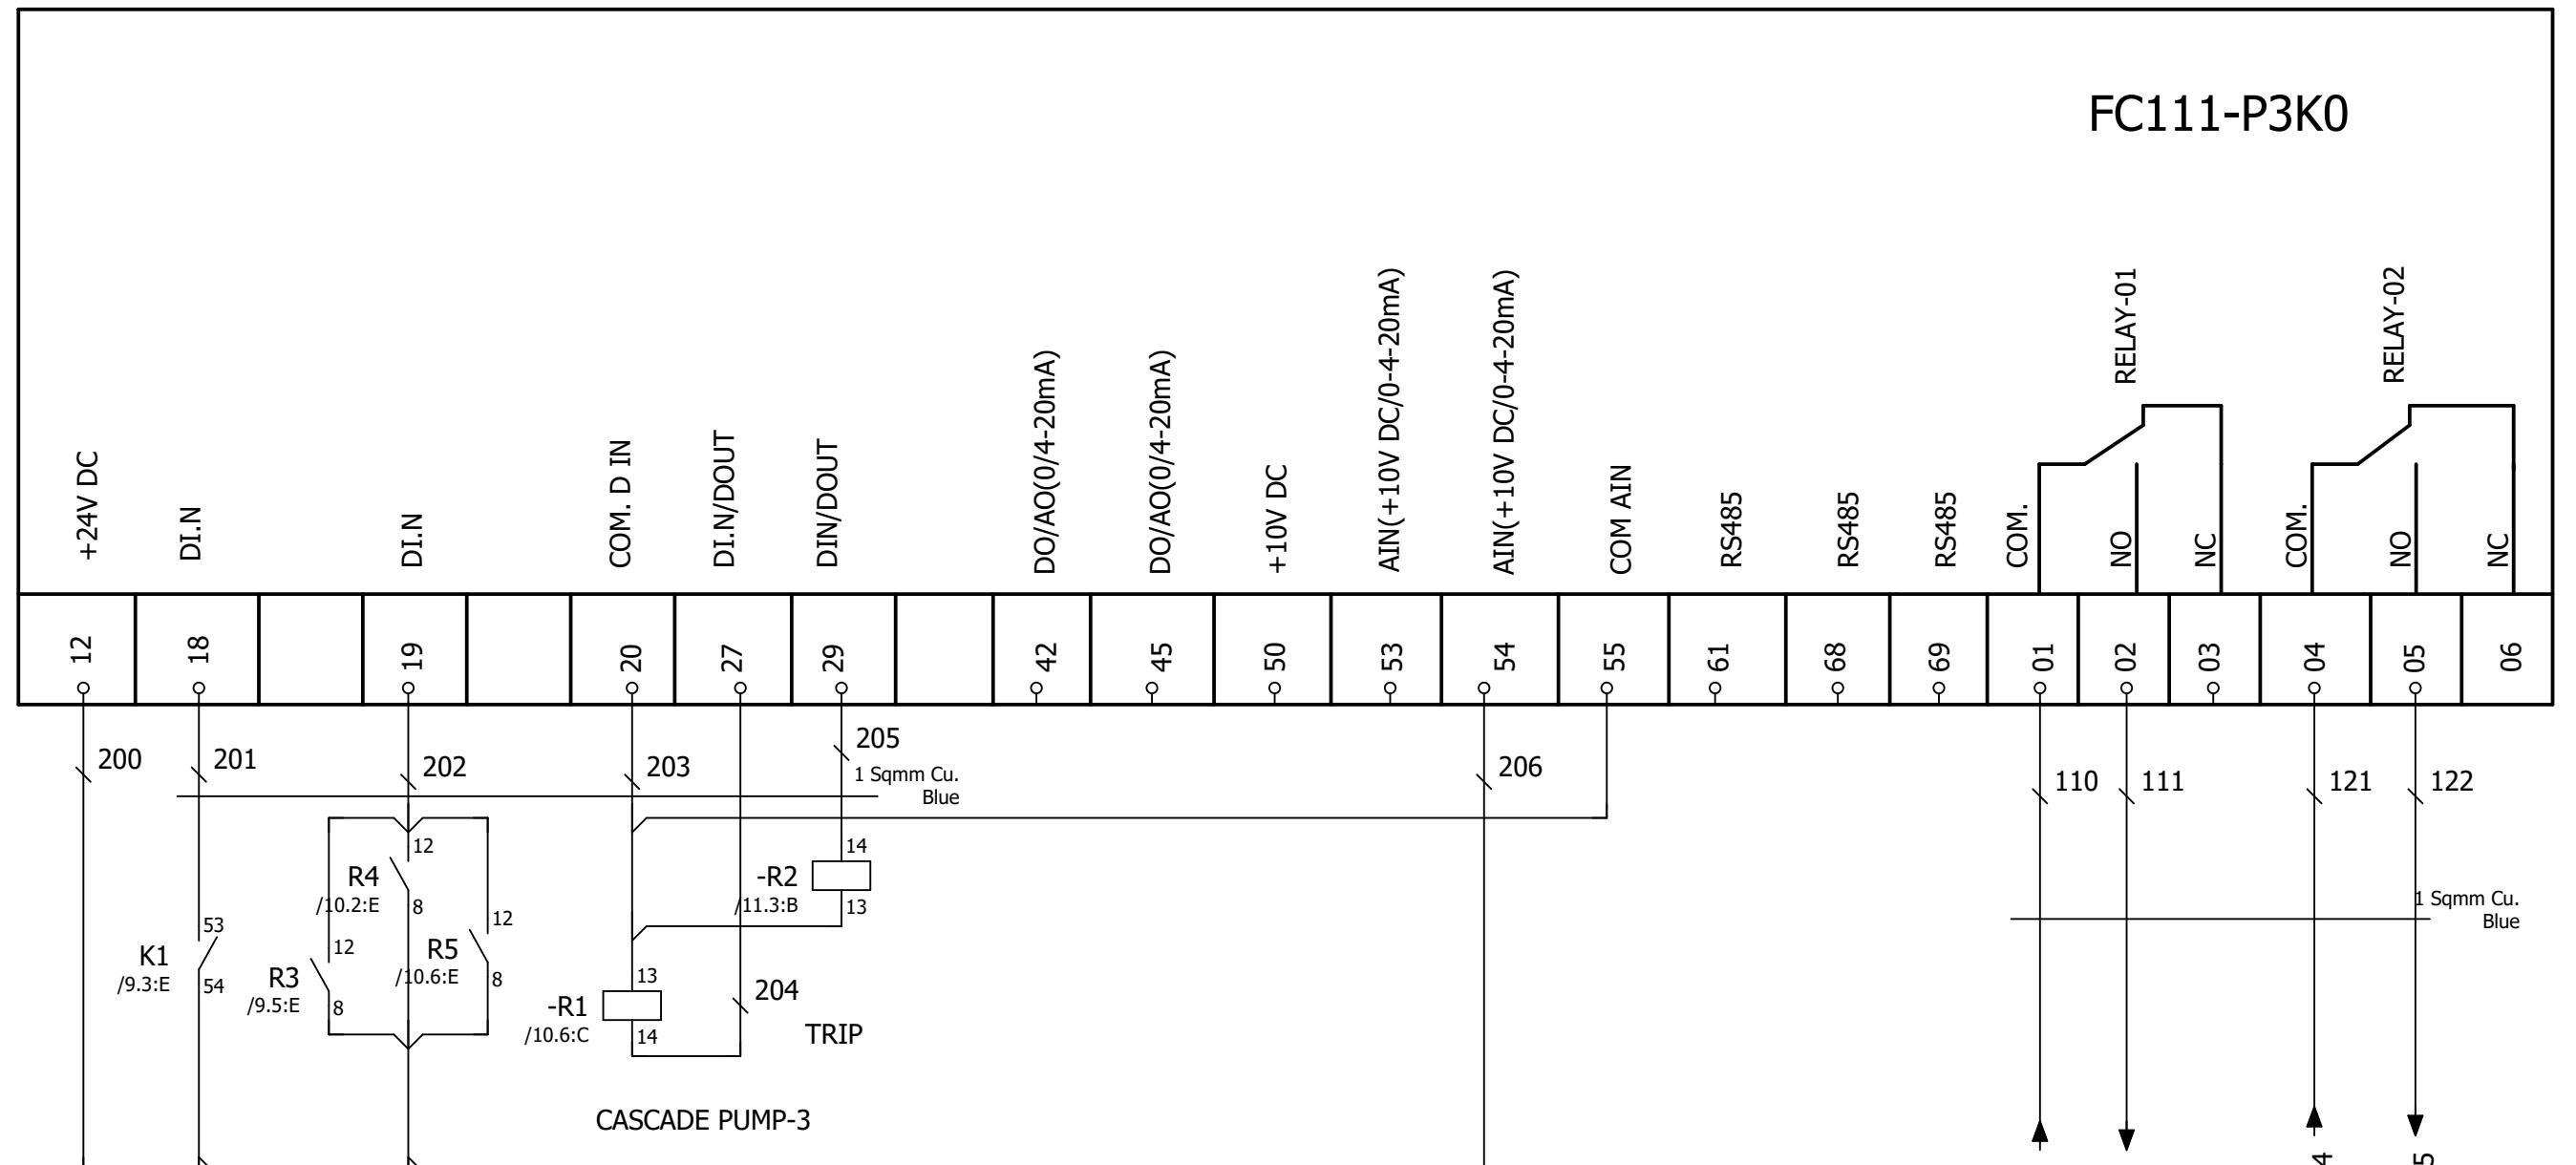

AB	ASBUILT	2025			
00	FOR APPROVAL	20/2017	DH	MP	MP
REV NO	REVISION	WEEK / YEAR	DWN BY	CHKD BY	APPD BY



Danfoss Industries Pvt.Ltd.

Title
Application
Customer
End User

MASTER VFD SCHEMATIC
PUMP
AQUA GROUP

P.O.No. -PO-
Job.No. INOE2025
Dwg.No. DIPL-CPV01-0030

Rev Sheet
AB 12
Cont. 13